




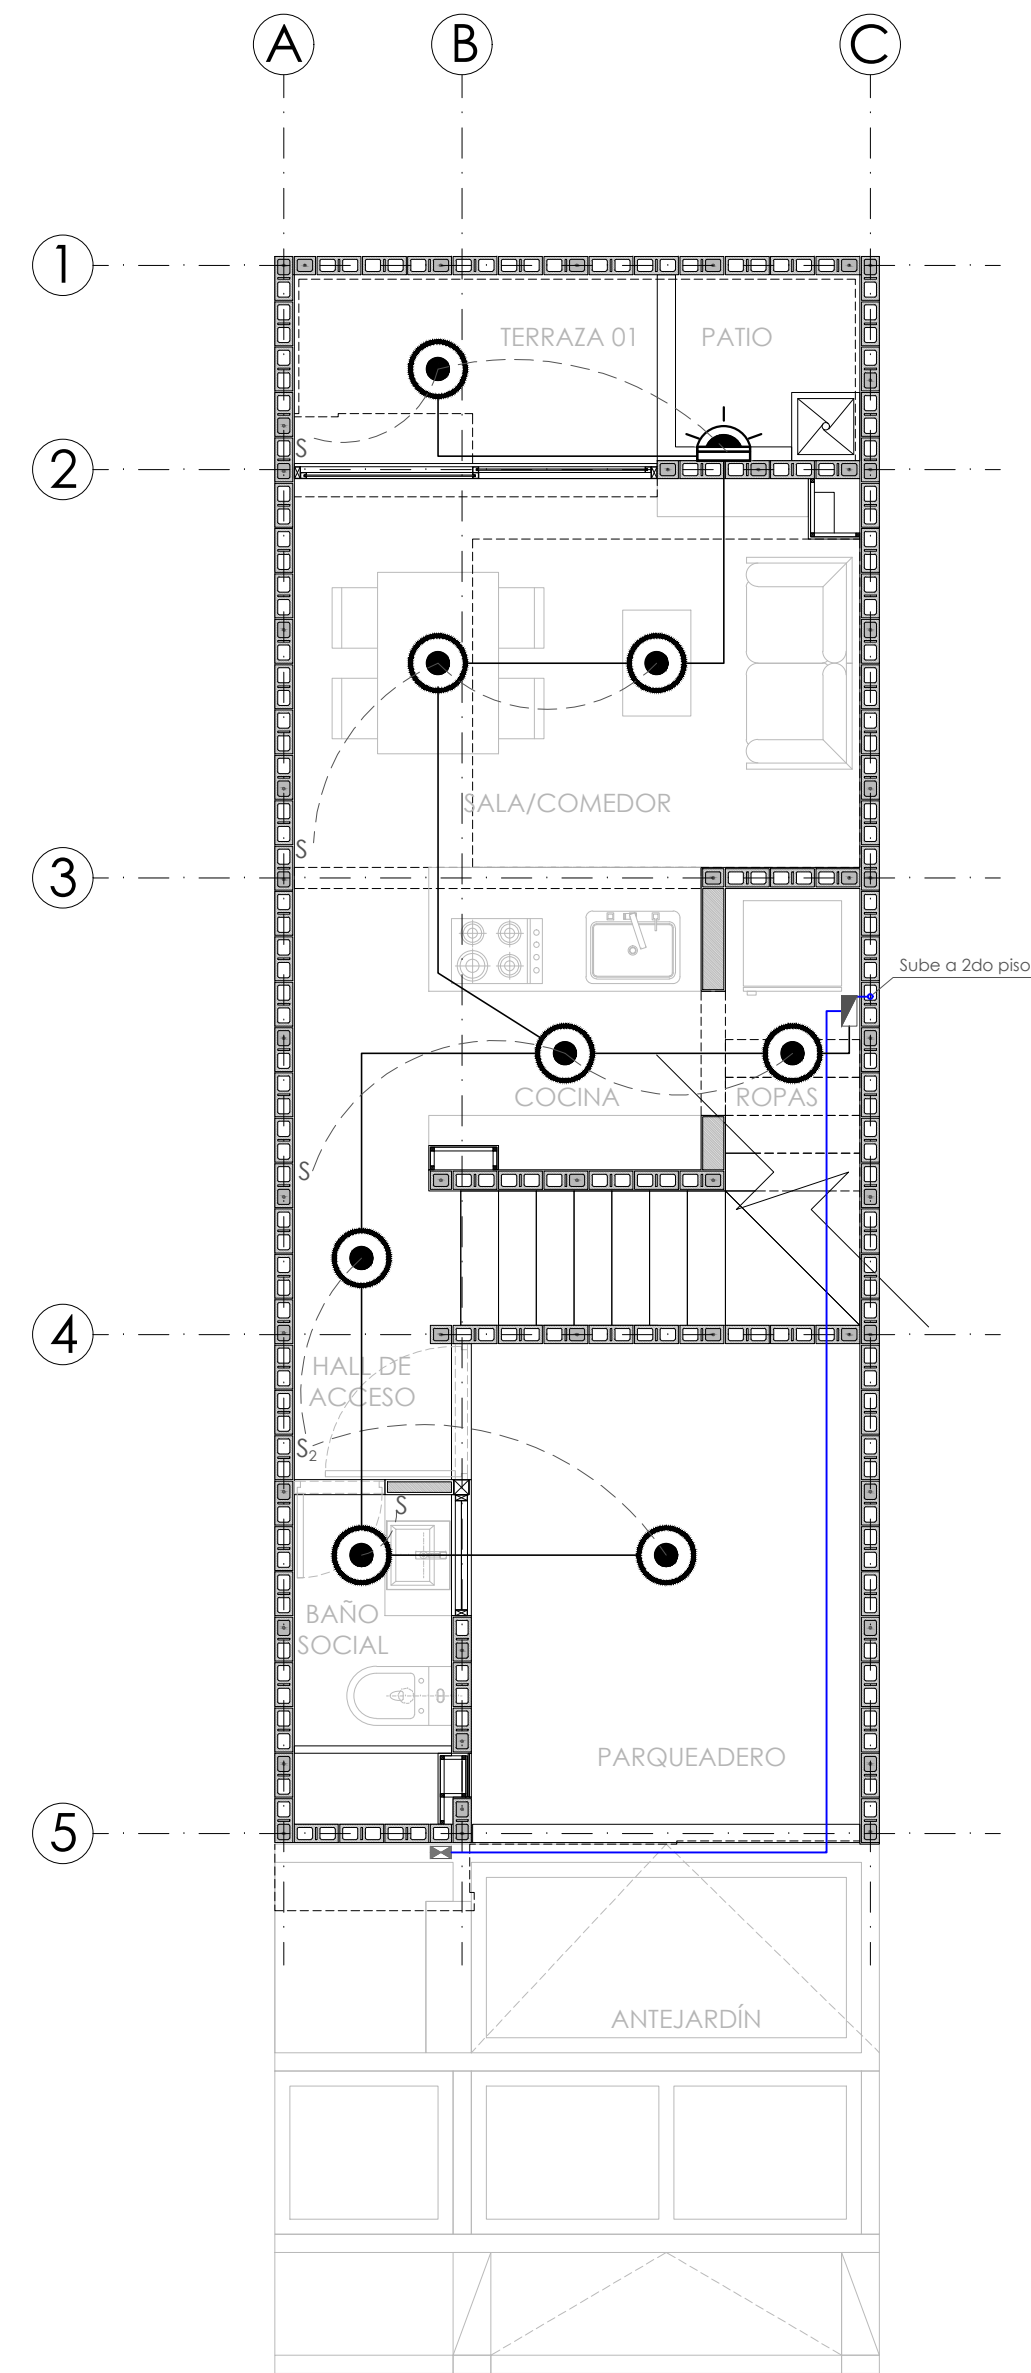

INSTALACIÓN ELÉCTRICA (ILUMINACIÓN) PISO 1 / ESC. 1:50

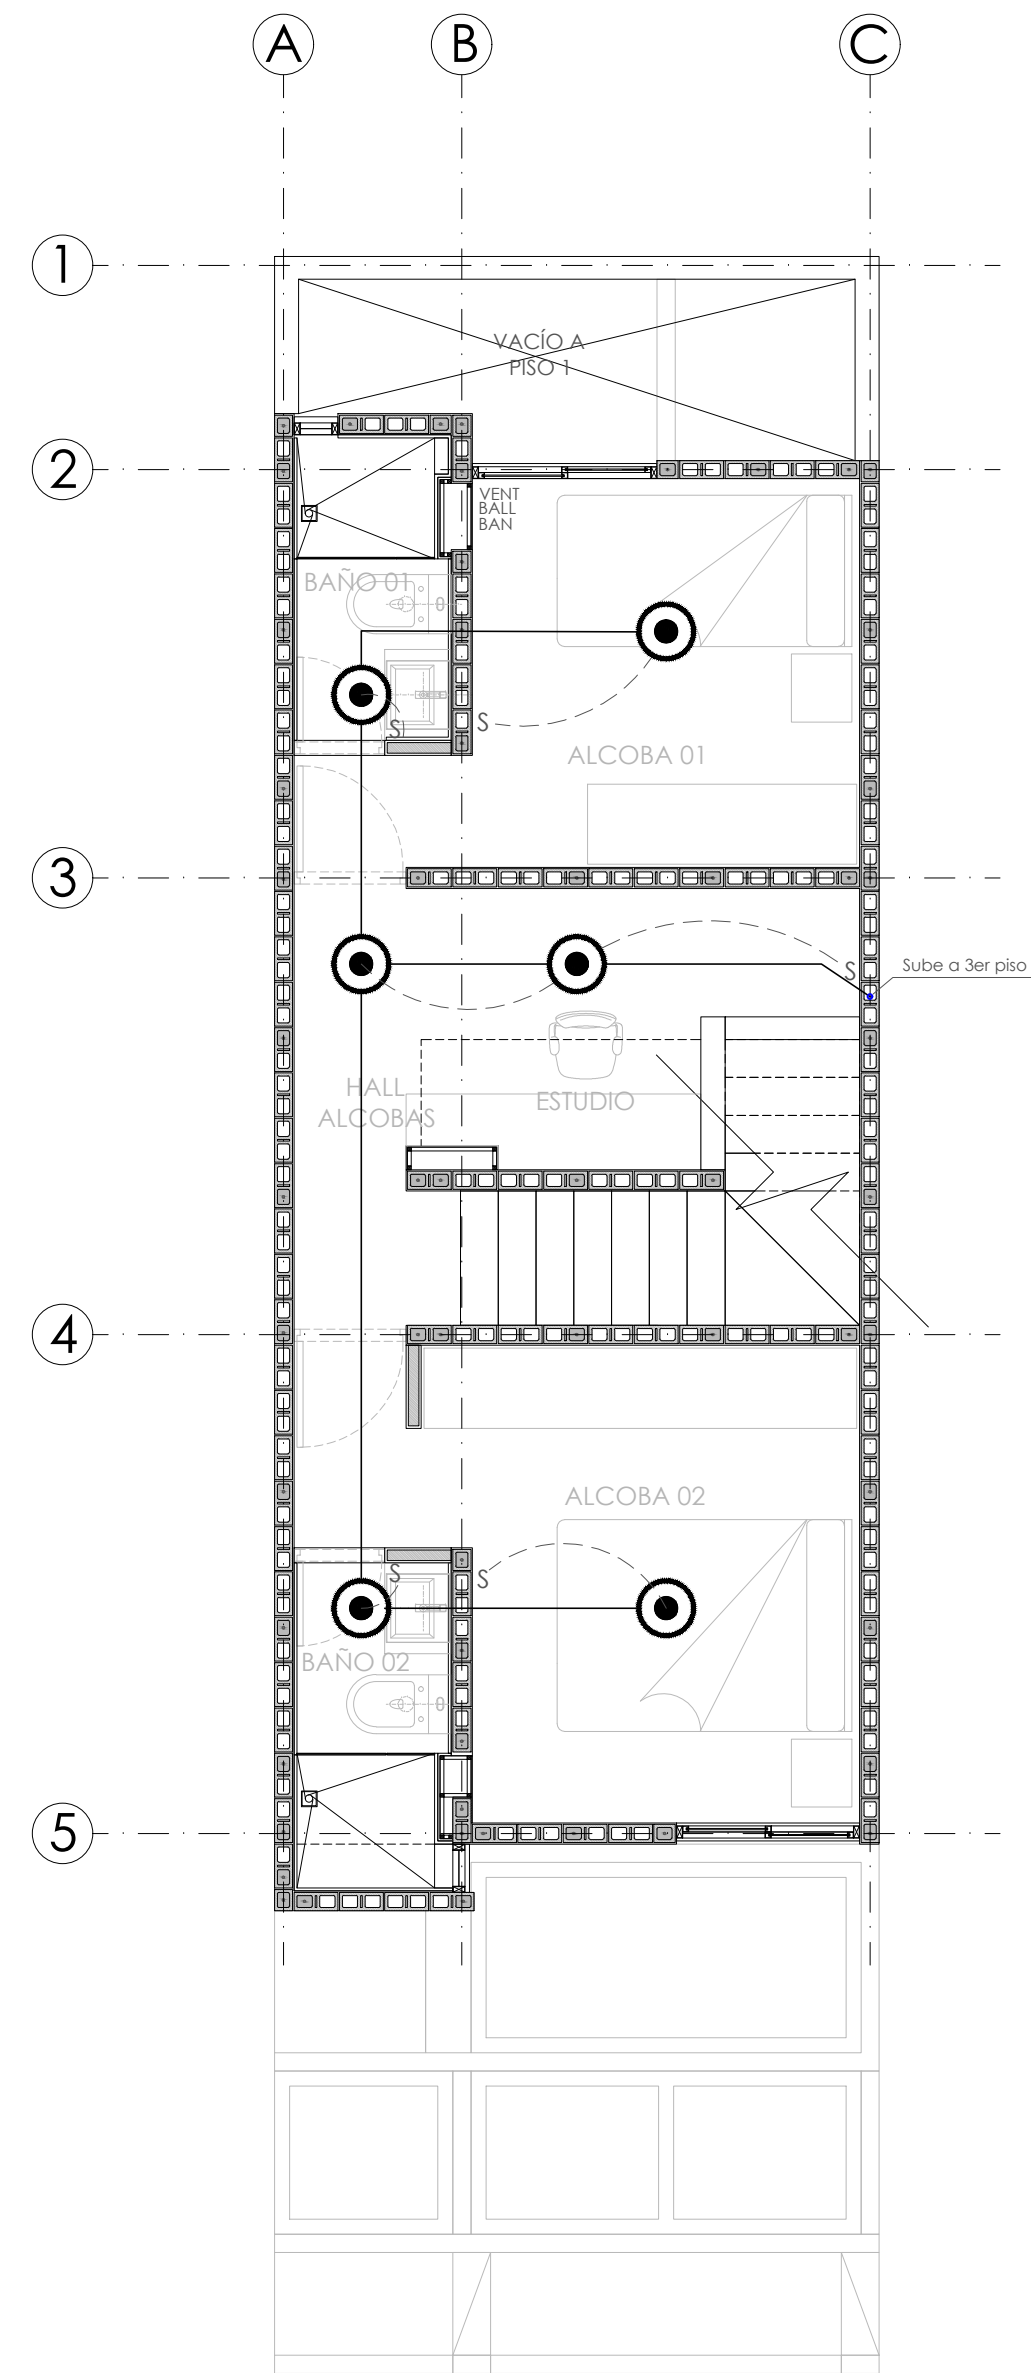

INSTALACIÓN ELÉCTRICA (ILUMINACIÓN) PISO 2 / ESC. 1:50

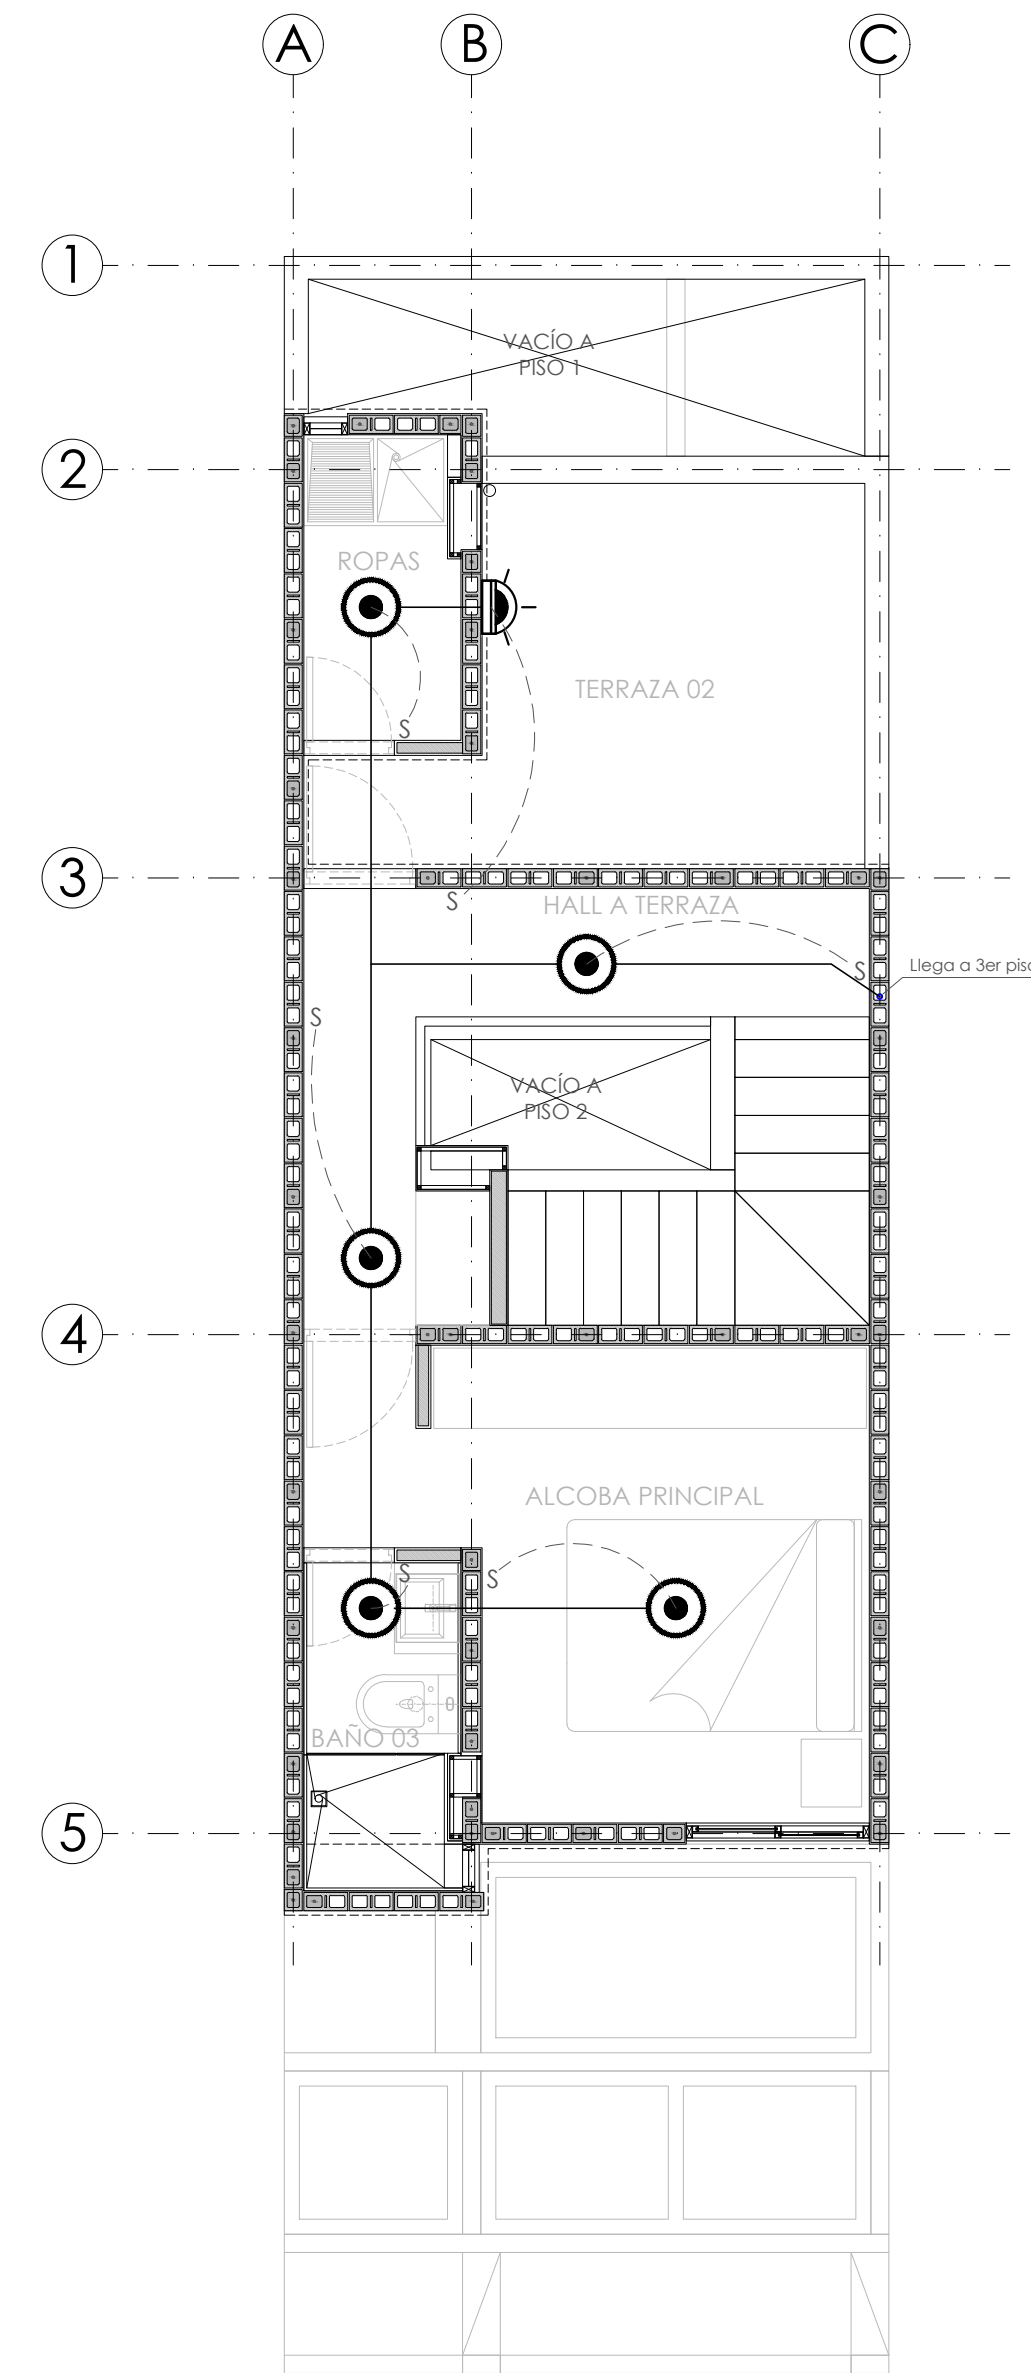

INSTALACIÓN ELÉCTRICA (ILUMINACIÓN) PISO 3 / ESC. 1:50

CONVENCIONES	
	TUBERIA POR CIELO
	TUBERIA POR PISO
	TUBERIA TELEVISION
	LINEA DE COMANDO
	CONTADOR
	TABLERO
	APAGADOR SENCILLO
	APAGADOR DOBLE
	APAGADOR CONMUTABLE
	APAGADOR CONMUTABLE DOBLE
	TOMACORRIENTE
	BALA TIPO LED (CIELO)
	LUMINARIA TIPO APLIQUE
	TOMA SALIDA DE TELEVISION
	CALENTADOR

PROYECTO	SANTA ELENA KM 3 VIA PASO DE LA BOLSA	
	GRUPO CAVSA ARQUITECTURA DISEÑO Y CONSTRUCCIÓN S.A.S	
	DAVID E. ARCILA DANIELA MELO EIDER M. RODRIGUEZ	
	INST. ELÉCTRICA (ILUMINACIÓN) PISO 1 INST. ELÉCTRICA (ILUMINACIÓN) PISO 2 INST. ELÉCTRICA (ILUMINACIÓN) PISO 3	
DISEÑADORES	DAVID E. ARCILA DANIELA MELO EIDER M. RODRIGUEZ	
	INST. ELÉCTRICA (ILUMINACIÓN) PISO 1 INST. ELÉCTRICA (ILUMINACIÓN) PISO 2 INST. ELÉCTRICA (ILUMINACIÓN) PISO 3	
	SUDOL SOLUCIONES URBANÍSTICAS COLOMBIA	
	SUDOL SOLUCIONES URBANÍSTICAS COLOMBIA	
PROPIETARIO	SUDOL SOLUCIONES URBANÍSTICAS COLOMBIA	
	SUDOL SOLUCIONES URBANÍSTICAS COLOMBIA	
	SUDOL SOLUCIONES URBANÍSTICAS COLOMBIA	
	SUDOL SOLUCIONES URBANÍSTICAS COLOMBIA	
OBSERVACIONES	SUDOL SOLUCIONES URBANÍSTICAS COLOMBIA	
	SUDOL SOLUCIONES URBANÍSTICAS COLOMBIA	
	SUDOL SOLUCIONES URBANÍSTICAS COLOMBIA	
	SUDOL SOLUCIONES URBANÍSTICAS COLOMBIA	