



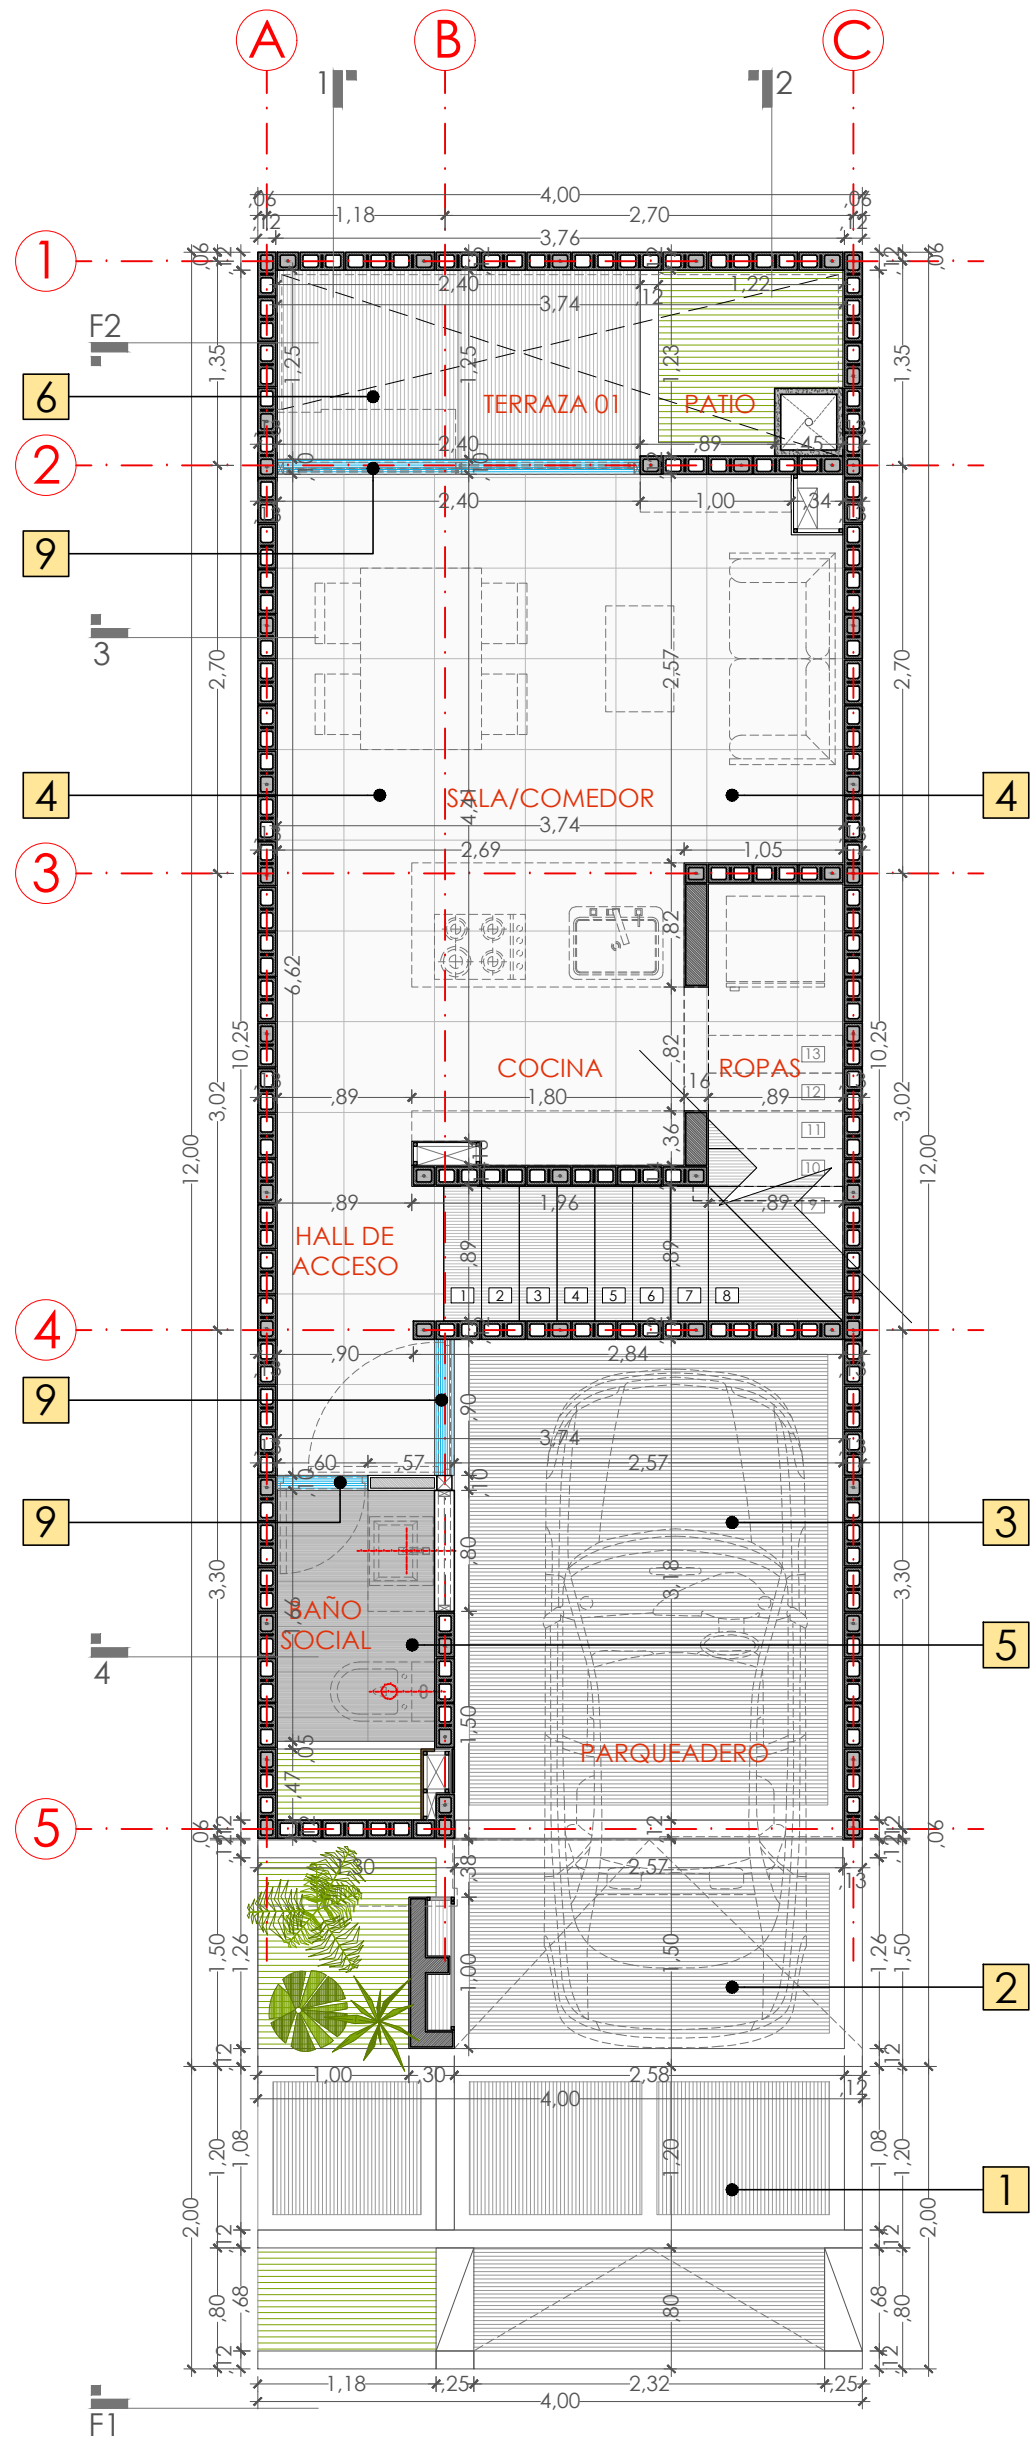


- 1 Andén en concreto escobillado con dilataciones
Área: 4.80m²
- 2 Rampa de acceso en concreto escobillado con dilataciones
Área: 4.05m²
- 3 Piso - parqueadero en concreto escobillado con dilataciones
Área: 8.17m²
- 4 Porcelanato color gris claro
Medidas: 60x60cm
Área: 18.74m²
- 5 Piso en cerámica zonas húmedas
Medidas: 30x60cm
Área: 1.72m²
- 6 Piso en concreto pulido
Área: 3.00m²
- 7 Piso en cerámica áreas exteriores
Medidas: 45x45cm
Área: No aplica
- 8 Impermeabilización materas
Área: No aplica
- 9 Cenefa de dilatación
ML: 3.90mts

PLANTA PISOS - PISO 1 / ESC. 1:50

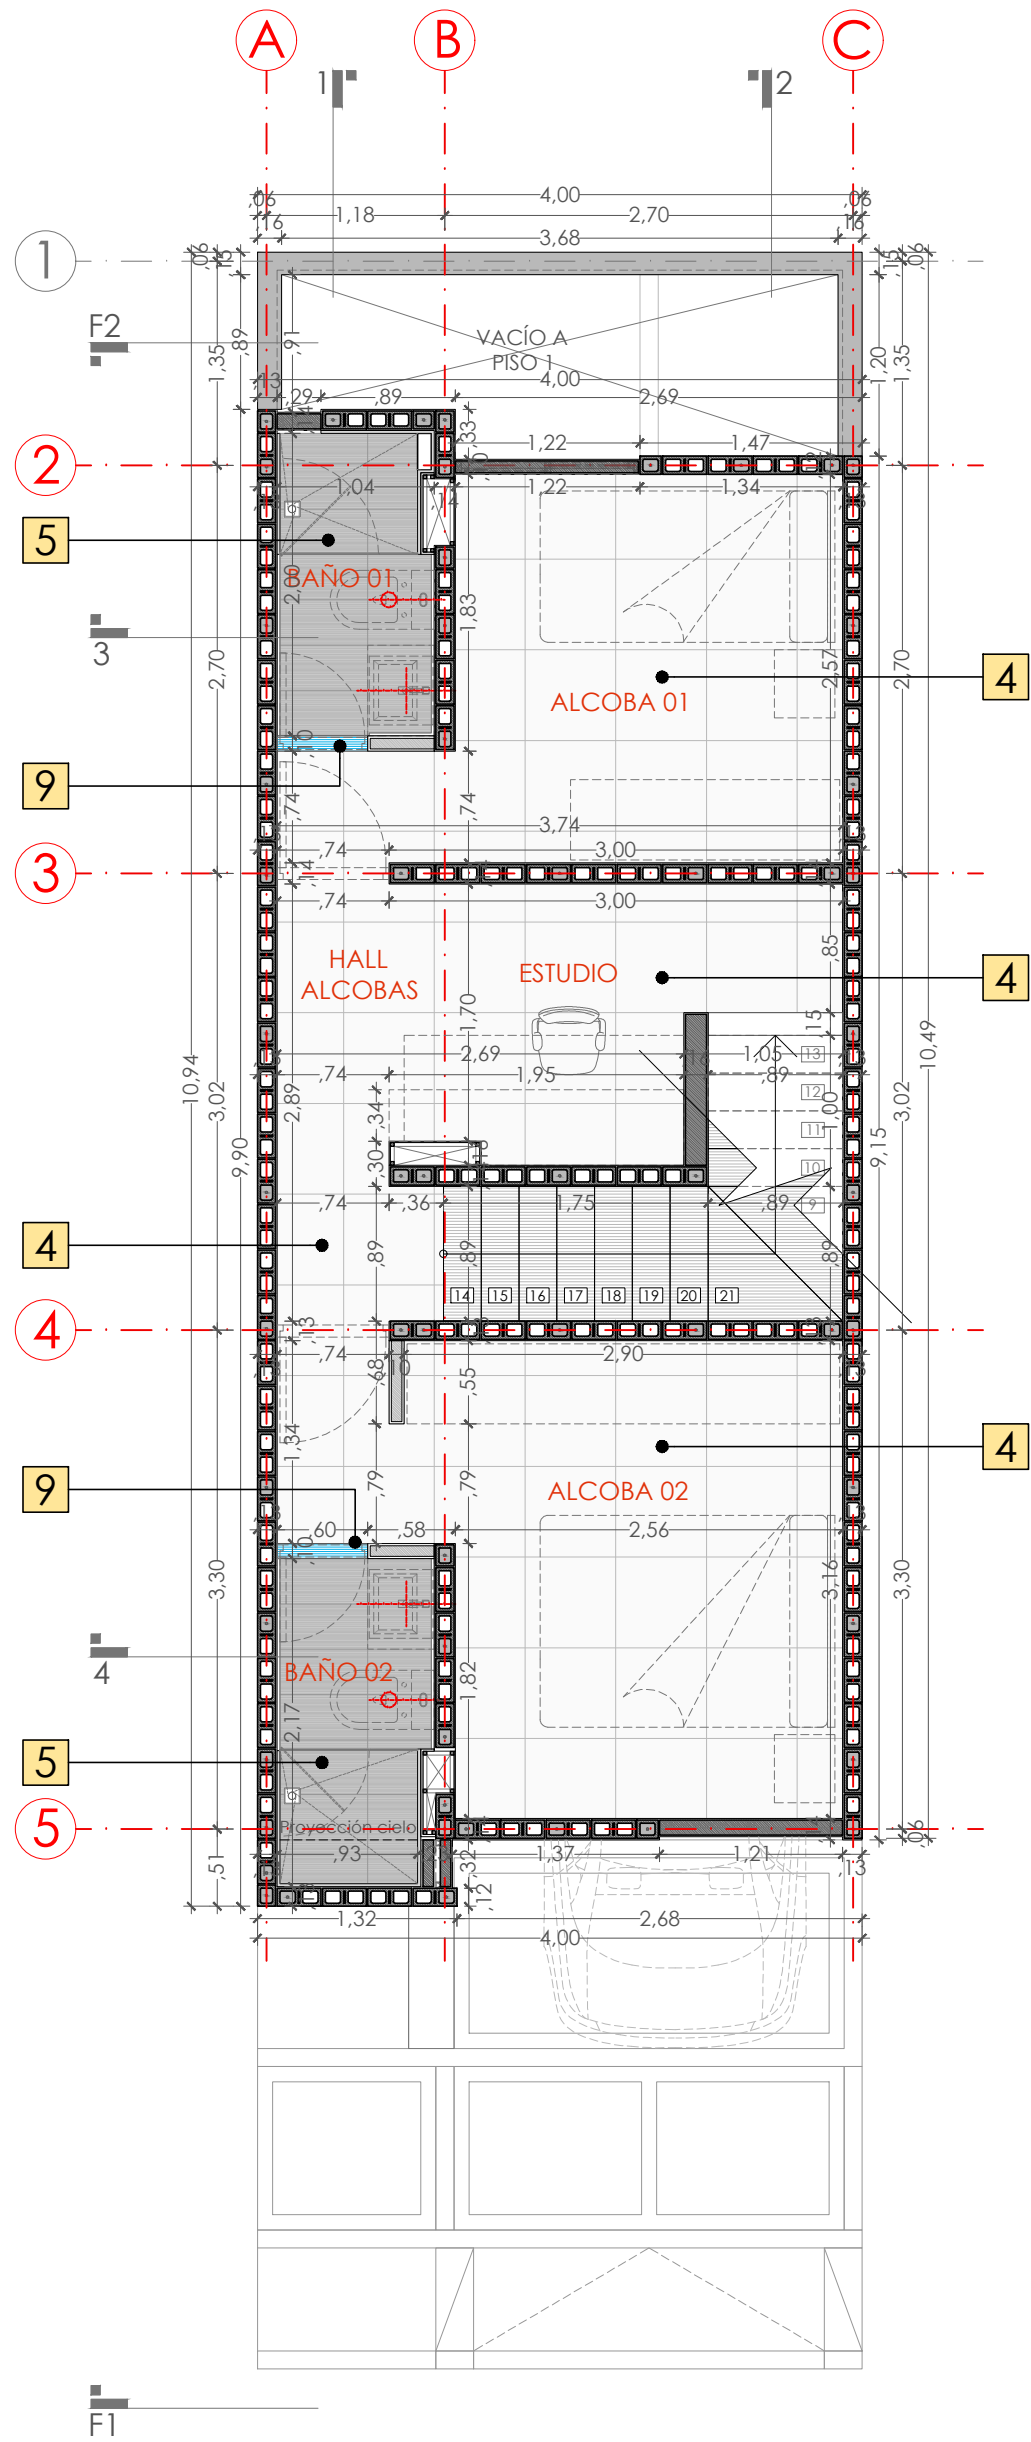

- 1 Andén en concreto escobillado con dilataciones
Área: No aplica
- 2 Rampa de acceso en concreto escobillado con dilataciones
Área: No aplica
- 3 Piso - parqueadero en concreto escobillado con dilataciones
Área: No aplica
- 4 Porcelanato color gris claro
Medidas: 60x60cm
Área: 24.15m²
- 5 Piso en cerámica zonas húmedas
Medidas: 30x60cm
Área: 4.16m²
- 6 Piso en concreto pulido
Área: No aplica
- 7 Piso en cerámica áreas exteriores
Medidas: 45x45cm
Área: No aplica
- 8 Impermeabilización materas
Área: No aplica
- 9 Cenefa de dilatación
ML: 1.20mts

PLANTA PISOS - PISO 2 / ESC. 1:50

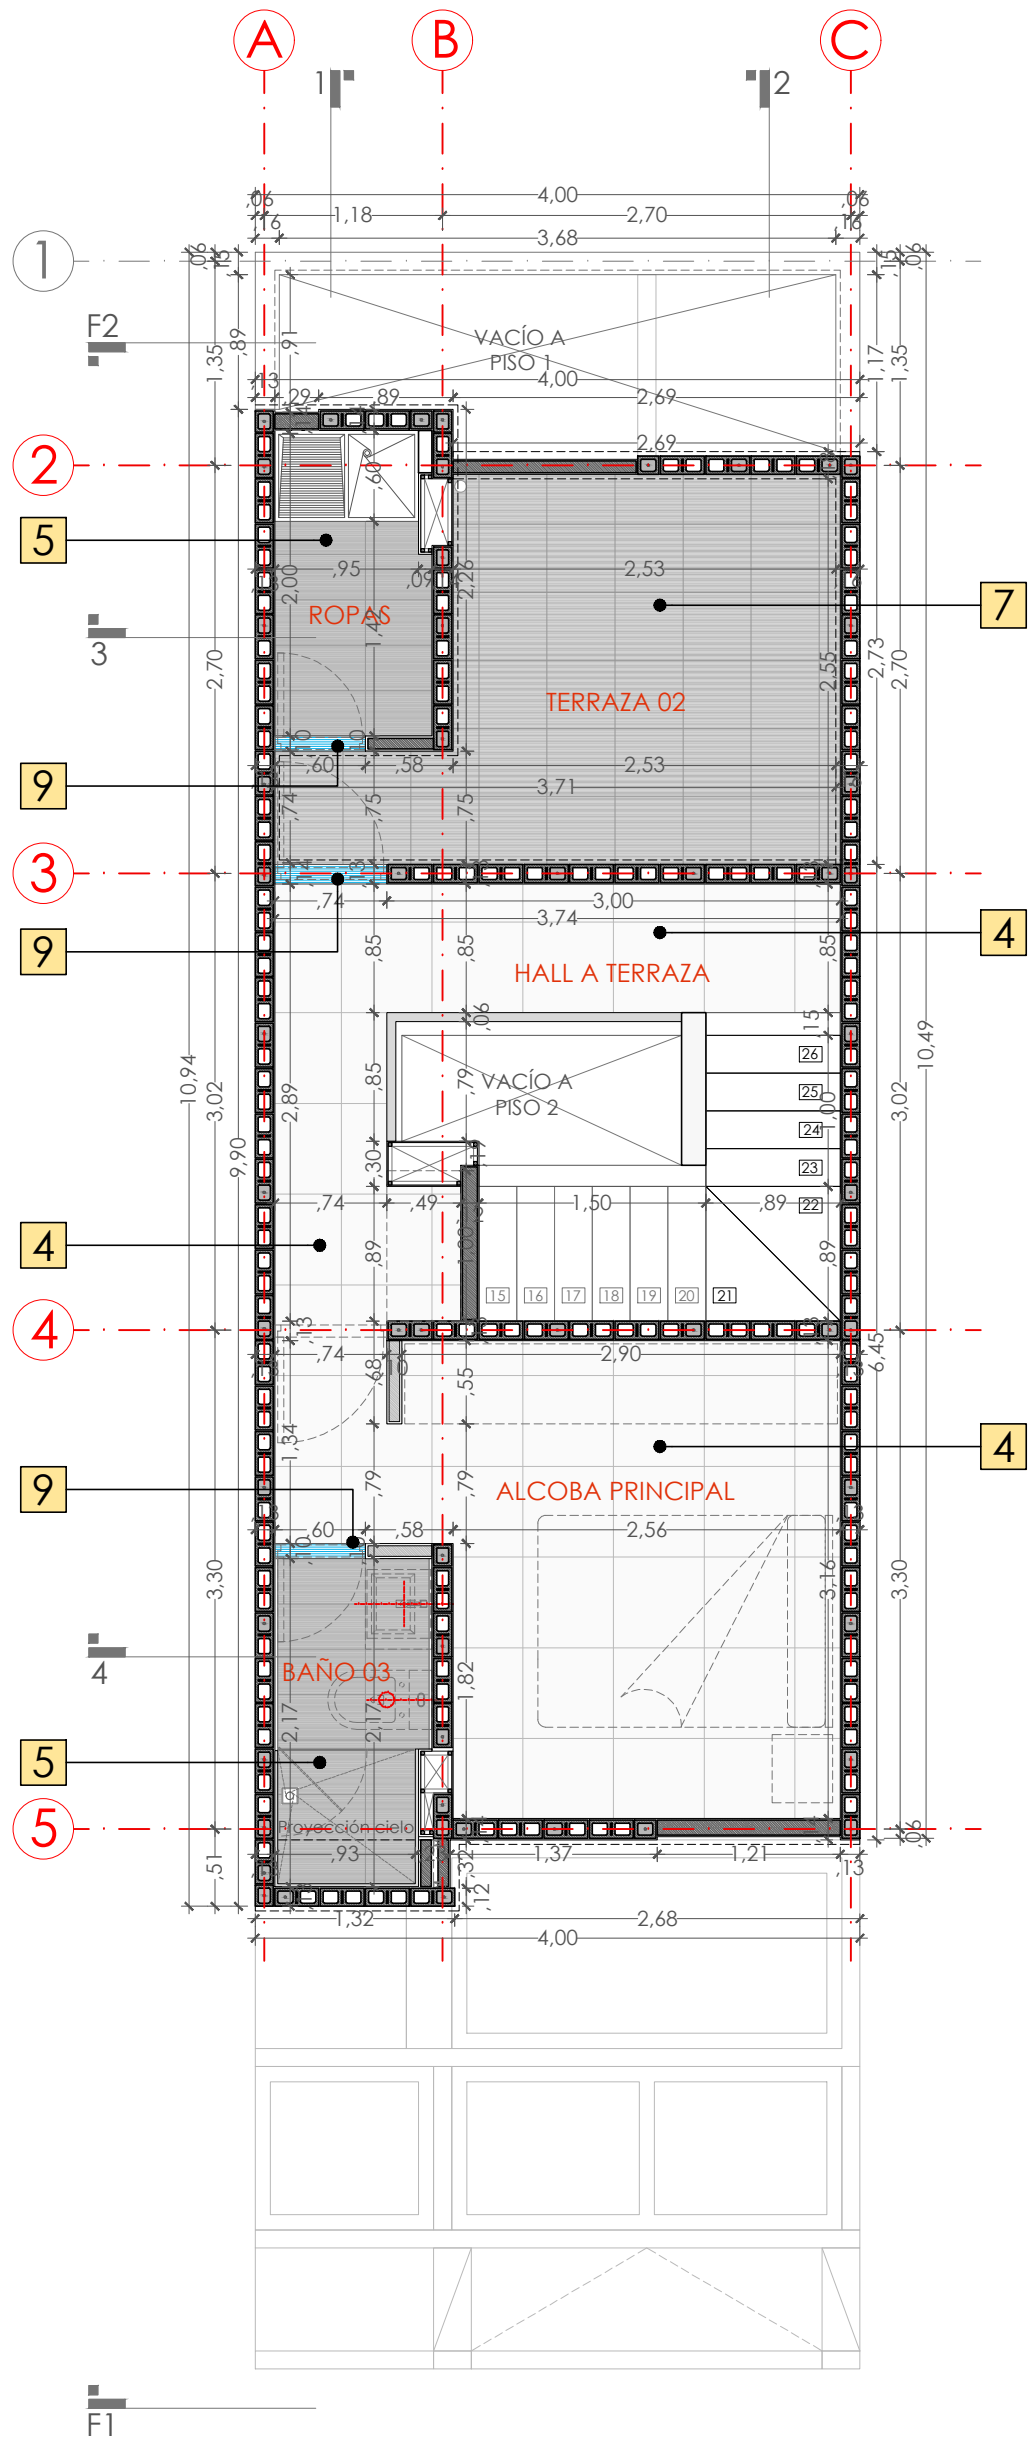

- 1 Andén en concreto escobillado con dilataciones
Área: No aplica
- 2 Rampa de acceso en concreto escobillado con dilataciones
Área: No aplica
- 3 Piso - parqueadero en concreto escobillado con dilataciones
Área: No aplica
- 4 Porcelanato color gris claro
Medidas: 60x60cm
Área: 14.83m²
- 5 Piso en cerámica zonas húmedas
Medidas: 30x60cm
Área: 4.16m²
- 6 Piso en concreto pulido
Área: No aplica
- 7 Piso en cerámica áreas exteriores
Medidas: 45x45cm
Área: 7.48m²
- 8 Impermeabilización materas
Área: No aplica
- 9 Cenefa de dilatación
ML: 1.94mts

PLANTA PISOS - PISO 3 / ESC. 1:50