
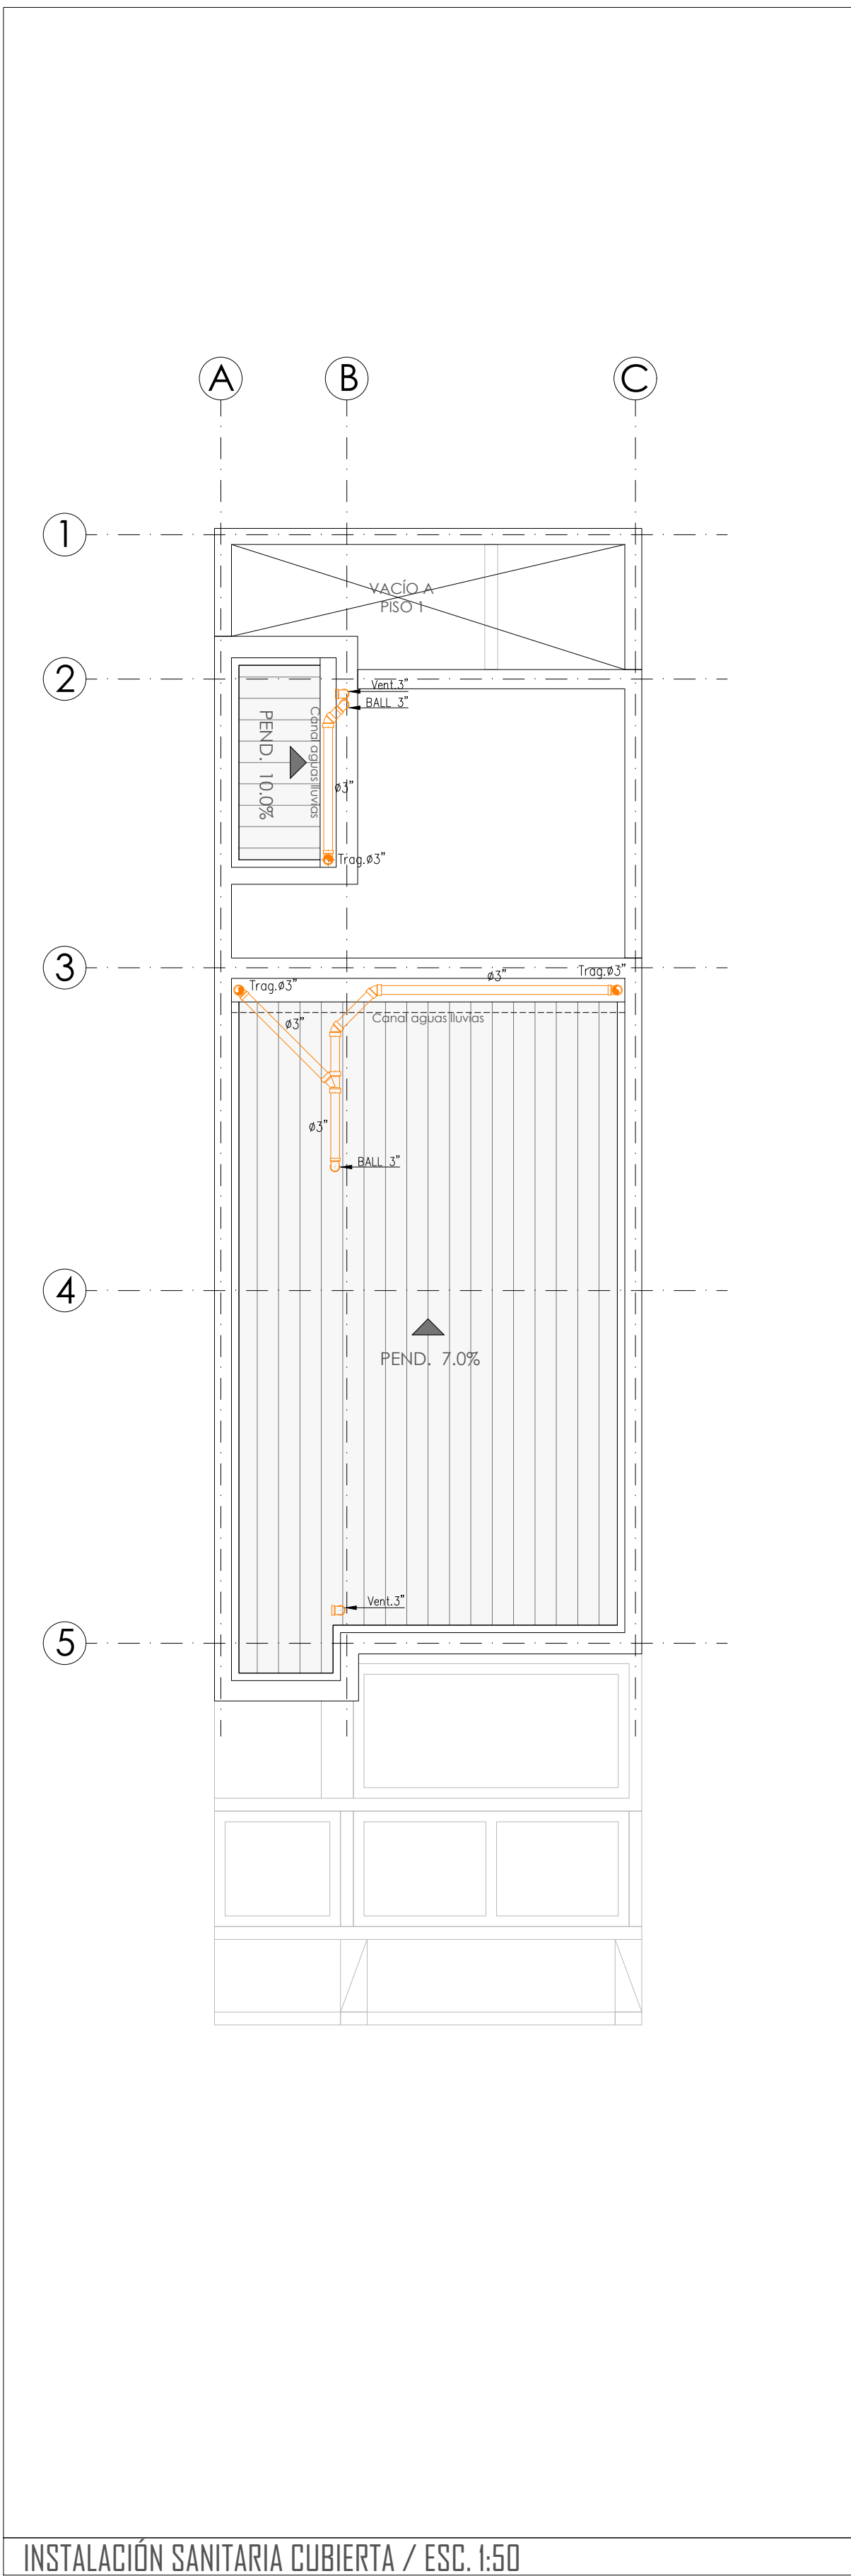
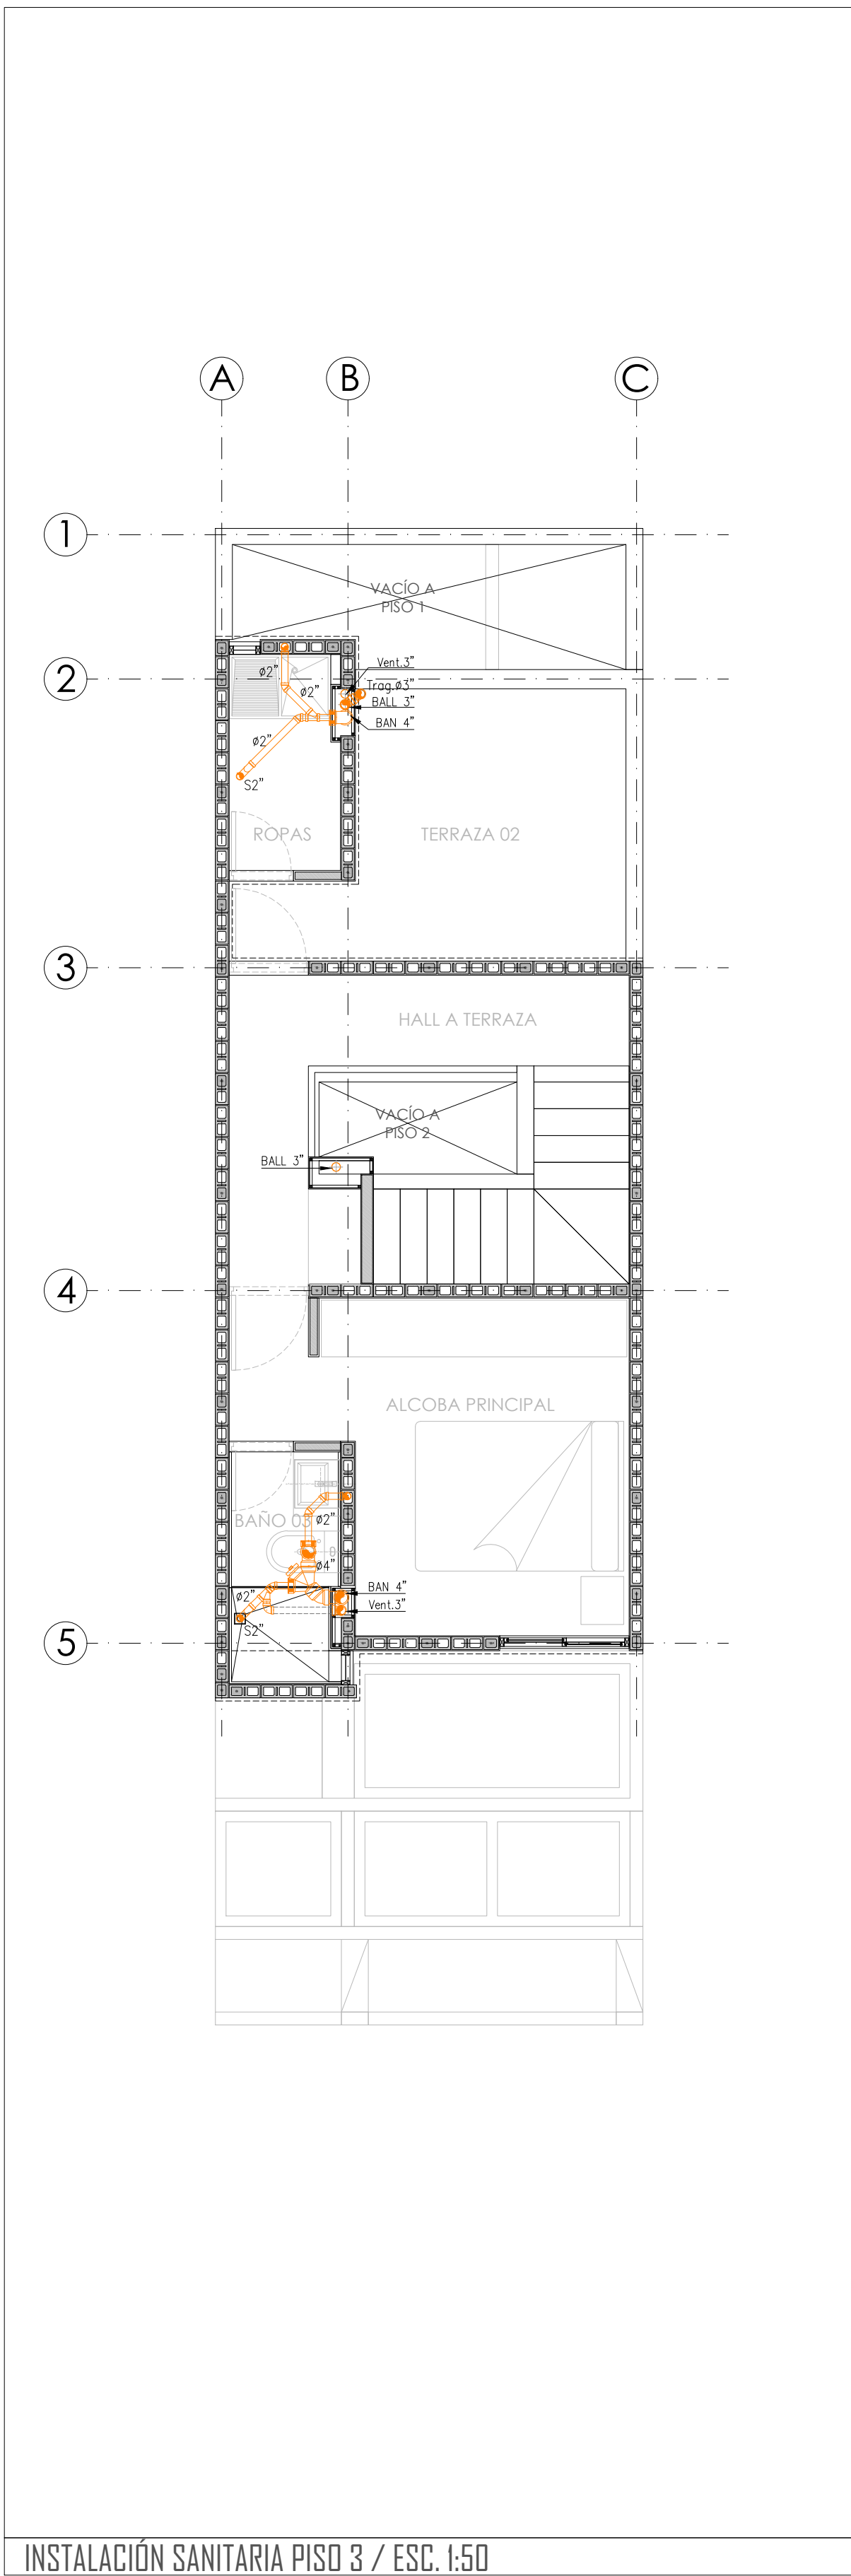
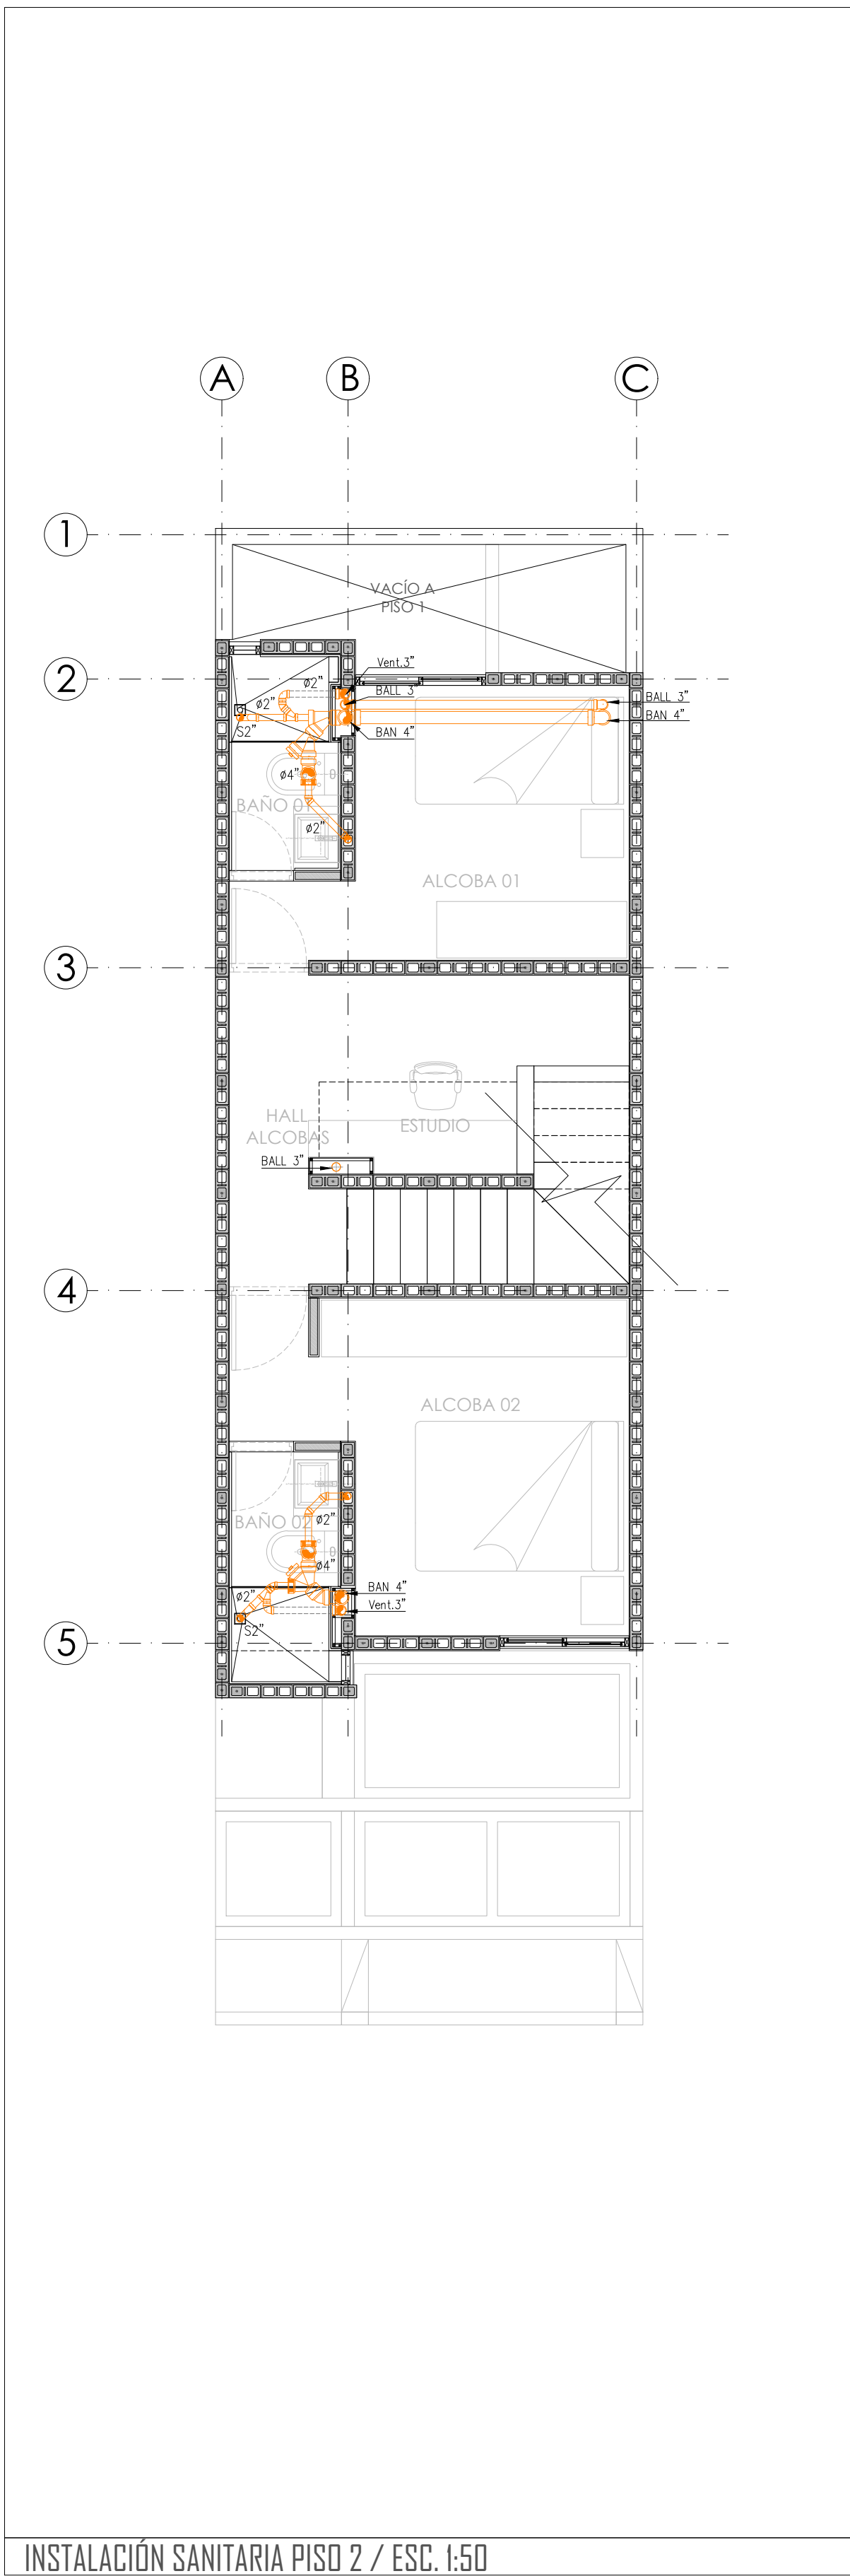


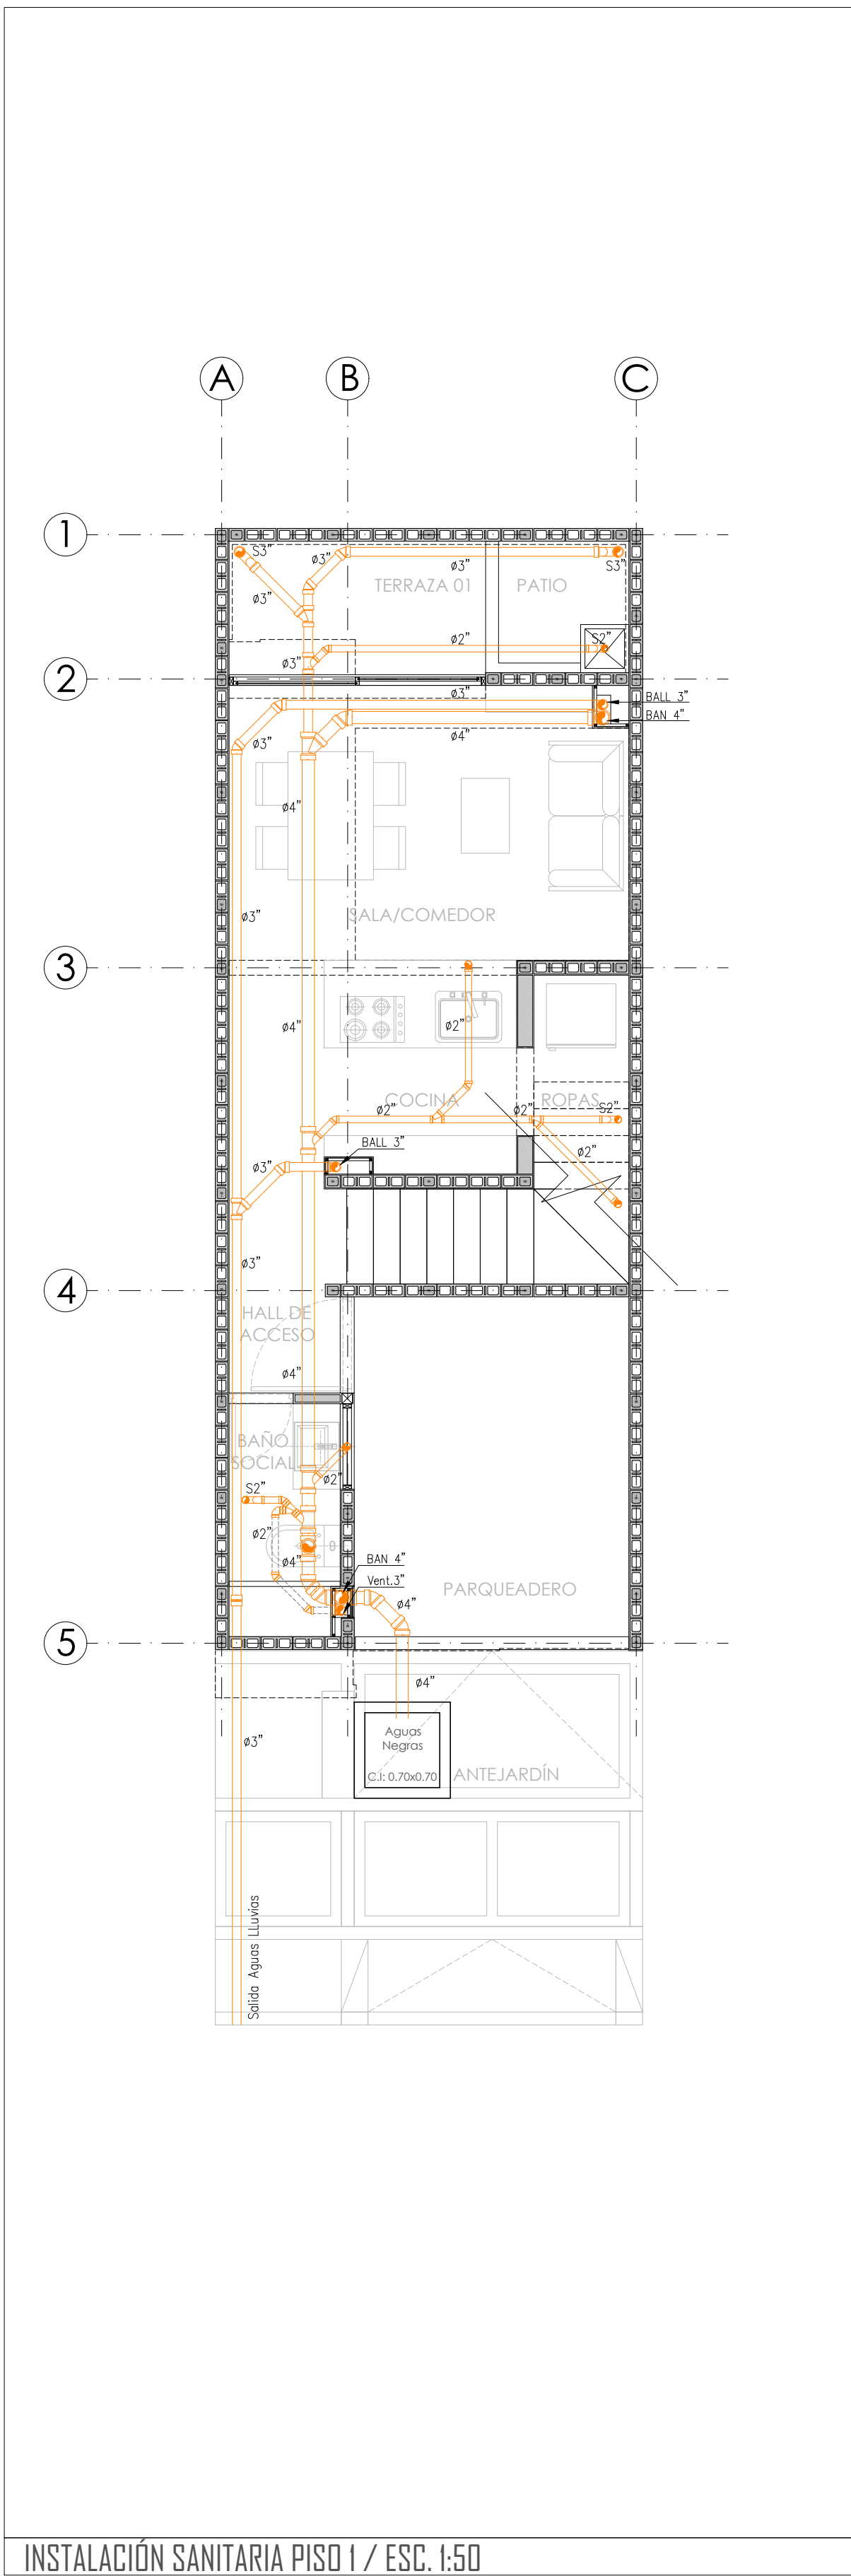

GRUPO CAVSA	PROYECTO	SANTA ELENA KM 3 VÍA PASO DE LA BOLSA	DISEÑA		DISEÑADORES	CONTENIDO	PROPIETARIO	OBSERVACIONES	PLANO ARQ.	12	08 - 10 - 2020 ESC. INDICADA
GRUPO CAVSA ARQUITECTURA DISEÑO Y CONSTRUCCIÓN S.A.S		DAVID E. ARCILA DANIELLA MELO EIDER M. RODRIGUEZ		INSTALACIÓN SANITARIA PISO 1 INSTALACIÓN SANITARIA PISO 2 INSTALACIÓN SANITARIA PISO 3 INSTALACIÓN SANITARIA CUBIERTA	SUDOL SOLUCIONES URBANÍSTICAS COLOMBIA						